Gobierno Municipal
CORONANGO
2024-2027
Tú confianza, nos lleva al progreso

FOLIO: 0019

DIRECCION DE DESARROLLO URBANO, SUSTENTABILIDAD, ORDENAMIENTO TERRITORIAL E IMAGEN URBANA

AYUNTAMIENTO DEL MUNICIPIO DE CORONANGO 2024-2027

CONSTANCIA DE ALINEAMIENTO Y NUMERO OFICIAL

N° DE OFICIO: **ALI-087-2024**

COMERCIAL IAC, S.A. DE C.V. (ARRENDATARIO).

DATOS GENERALES							
CALLE:	LATERAL AUTOPISTA MÉXICO PUEBLA KM 115						
LOCAL:	M-1	MANZANA:	-	N° ACTUAL	1001	JUNTA AUXILIAR:	SAN FRANCISCO OCOTLAN
MUNICIPIO:	CORONANGO, PUEBLA.						
SUPERFICIE:	194.00 M2					CUENTA PREDIAL	U-118251.
MEDIDAS Y COLINDANCIAS:							
AL NORTE:	EN 15.07 M., CON ACCESO Y PASILLO DE LA PLAZA.						
AL SUR:	EN 15.07 M COLINDA CON LOCAL COMERCIAL.						
AL OESTE:	EN 12.75 M COLINDA CON PASILLO DE LA PLAZA.						
AL ESTE:	EN 12.75 M COLINDA CON LOCAL COMERCIAL.						

ALINEAMIENTO Y NUMERO OFICIAL					
ESTA DIRECCIÓN POR MEDIO DEL AREA CORRESPONDIENTE SEÑALADO EL					
CALLE:	LATERAL AUTOPISTA MÉXICO PUEBLA	N° OFICIAL:	1001	LOCAL:	M-1
FRACCIONAMIENTO O CONJUNTO HABITACIONAL	-				
MUNICIPIO:	CORONANGO, PUEBLA	JUNTA AUXILIAR:	SAN FRANCISCO OCOTLÁN		
EL PREDIO SE UBICA EN: **AREA COMERCIAL**					

OBSERVACIONES PARTICULARES:

CONTRATO DE ARRENDAMIENTO SIMPLE FIRMADO POR **ARRENDADOR:** PARQUES INDUSTRIALES DE PUEBLA, S.A. DE C.V., **ARRENDATARIO:** COMERCIAL IAC S.A. DE C.V. **CON FECHA DE** 01 DE SEPTIEMBRE DE 2024 AL 31 DE AGOSTO DE 2027.

ACTA CONSTITUTIVA **LIBRO 851** INSTRUMENTO No. 32 227 NOTARÍA **NO. 215 DF, MÉXICO.**, DE FECHA **18 DE AGOSTO DE 2009**, CON FECHA DE INSCRIPCION EN EL REGISTRO PUBLICO Y DEL COMERCIO. **04 DE FEBRERO DE 2010**.

PODER NOTARIAL CON VOLUMEN No. 699, ESCRITURA No. 34 659, NOTARIA No. 65, LIC. JOSE LUIS MAZOY KURI, DE FECHA: 01 DE JUNIO DE 2018.

VIGENCIA UN AÑO

CON FUNDAMENTO EN DISPUESTO EN EL ARTÍCULOS 27 y 115 FRACCIÓN V INCISO F) DE LA CONSTITUCIÓN POLÍTICA DE LOS ESTADOS UNIDOS MEXICANOS; ARTÍCULOS 105 FRACCIÓN IV INCISO A) Y F) DE LA CONSTITUCIÓN POLÍTICA DEL ESTADO LIBRE Y SOBERANO DE PUEBLA; ARTÍCULOS 11 FRACCIÓN II, III, IX, XV, XVIII, 43, 47, 48, 58, 59, 60 FRACCIÓN III, DE LA LEY GENERAL DE ASENTAMIENTOS HUMANOS, ORDENAMIENTO TERRITORIAL Y DESARROLLO URBANO; ARTÍCULOS 12 FRACCIÓN IV, 16 FRACCIÓN I, VI, VII, XVIII, XXIX, 19, 43, 61, 67, 69, 86, 87, 90, 92, 102, 105, 106, 107, 108, 111, 112, 113, 119, 120, 122, 123 FRACCIÓN IV, 124, 125 FRACCIÓN IV Y VI, 126, 127 FRACCIÓN III Y 133 FRACCIÓN IV Y VI, DE LA LEY DE ORDENAMIENTO TERRITORIAL Y DESARROLLO URBANO DEL ESTADO DE PUEBLA; ARTÍCULOS 2, 3, 5, 6, 8 FRACCIÓN III, 12 FRACCIÓN I, II, III, 34, 36, 37 Y 38, DE LA LEY DE FRACCIONAMIENTOS Y ACCIONES URBANÍSTICAS DEL ESTADO LIBRE Y SOBERANO DE PUEBLA; ARTÍCULO 254, 256, 257, 284, 285, 286, 289, 290, 291, 292, 293, 294, 295, 297, 298, 303, 306, 307, 309, 317, 319, Y ARTÍCULO 450 DEL REGLAMENTO DE CONSTRUCCIONES PARA EL ESTADO DE PUEBLA; ARTICULO 1604, 1605, 1606, 1607, 1608, 1609, 1610, 1611, 1612, 1613, 1614, 1615 Y 1623 DEL REGLAMENTO DE ORDEN Y JUSTICIA CÍVICA MUNICIPAL DE CORONANGO. ASÍ COMO LO ESTABLECIDO EN EL PROGRAMA MUNICIPAL DE DESARROLLO URBANO SUSTENTABLE DE CORONANGO, ARTÍCULO 14 FRACCIÓN I DE LA LEY DE INGRESOS DEL MUNICIPIO DE CORONANGO PARA EL EJERCICIO FISCAL VIGENTE, LAS LICENCIAS, PERMISOS Y AUTORIZACIONES QUE EXPIDA LA AUTORIDAD MUNICIPAL, LOS DATOS PERSONALES RECABADOS SERÁN PROTEGIDOS, INCORPORADOS Y TRATADOS DE ACUERDO CON LO ESTABLECIDO EN LOS ARTÍCULOS 1, 26, 30 Y 31 DE LA LEY GENERAL DE PROTECCIÓN DE DATOS PERSONALES EN POSESIÓN DE SUJETOS OBLIGADOS; Y 7 DE LOS LINEAMIENTOS GENERALES DE PROTECCIÓN DE DATOS PERSONALES PARA EL SECTOR PÚBLICO. ASÍ MISMOS SE LE INFORMA QUE SUS DATOS NO PODRÁN SER DIFUNDIDOS SIN SU CONSENTIMIENTO EXPRESO, SALVO LAS EXCEPCIONES PREVISTAS EN LA LEY.

Gobierno Municipal
CORONANGO
2024 - 2027
Tu confianza, nos lleva al progreso

27 DE NOVIEMBRE DE 2024
ALINEAMIENTO N° DE OFICIO: ALI-087-2024

CROQUIS ESQUEMATICO

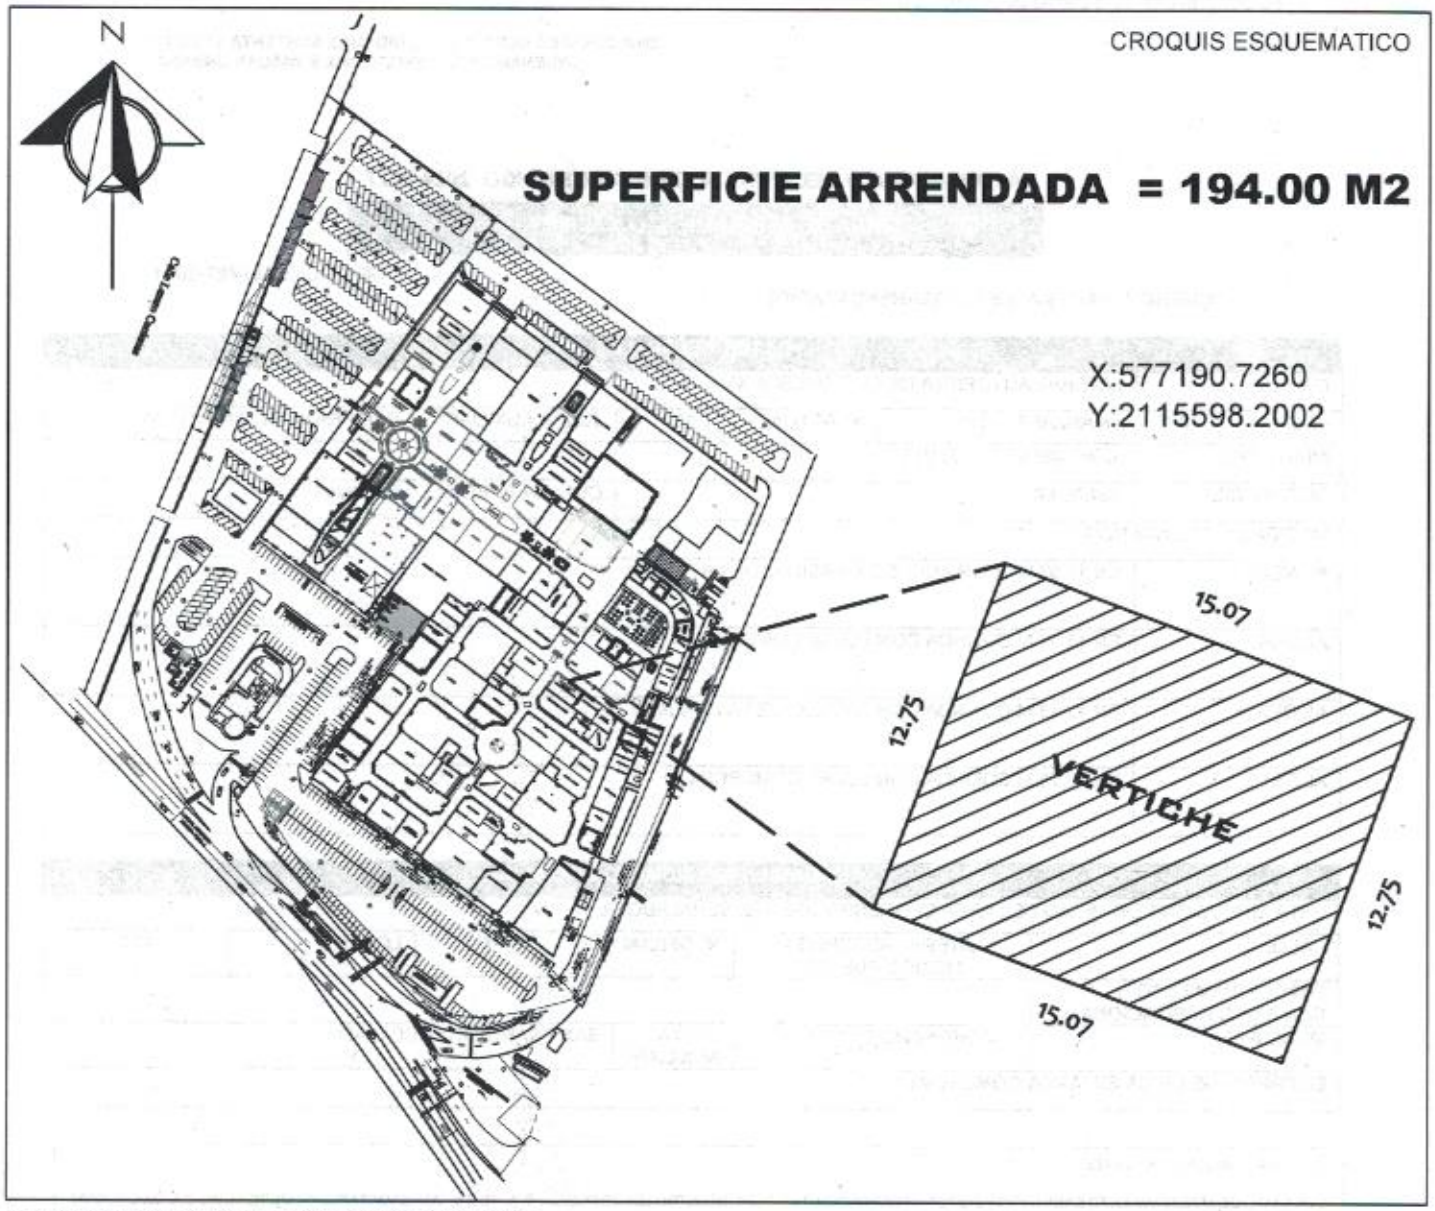

OBSERVACIONES ALINEAMIENTO Y NUMERO OFICIAL

-TÉCNICO URBANÍSTICO - NO CONSTITUYE NI CERTIFICA PROPIEDAD O POSESION CONSTANCIA DE APEO Y DESLINDE
-SE EXPIDE SIN PERJUICIO A TERCEROS
-SUPERFICIE, MEDIDAS Y COLINDANCIAS SON RESPONSABILIDAD DEL INTERESADO
-SE EXPIDE PARA CONOCIMIENTO DE NOMENCLATURA Y TRAMITES NOTARIALES
-DOCUMENTO DE CARÁCTER TÉCNICO
-INFORMACIÓN PROPORCIONADA BAJO PROTESTA DE DECIR VERDAD POR EL INTERESADO
-SUJETO A LAS DISPOSICIONES TÉCNICO NORMATIVAS REGLAMENTARIAS VIGENTES EN MATERIA DE PLANEACIÓN DE DESARROLLO URBANO.
-EL NÚMERO OFICIAL ASIGNADO SE COLOCARÁ AL FRENTE DE LOS INMUEBLES UNIDOS
-ESTE ALINEAMIENTO ES EXPEDIDO EN BASE A UN LEVANTAMIENTO FOTOGRAFICO REALIZADO, FIRMADO POR EL INTERESADO Y D.R.O.
-EN CASO DE EXISTIR ALGUNA RECLAMACIÓN, INCONSISTENCIA O DEFICIENCIA EN EL CATASTRO, R.P.P, EL NOTARIO PUBLICO, EL ADQUIRIENTE O CUALQUIER DEPENDENCIA ADMINISTRATIVA SERÁN EXCLUSIVA RESPONSABILIDAD DEL SOLICITANTE O EN SU CASO EL PROPIETARIO
-EL PRESENTE ALINEAMIENTO SE REALIZA CONFORME ALA INFORMACION PROPORCIONADA POR EL INTERESADO, POR LO QUE CUALQUIEER ACLARQCION O CAMBIO SERA UNICAMENTE RESPONSABNILIDAD DEL MISMO
-ESTE CROQUIS Y No. OFICIAL SE REALIZO EN BASE AL LEVANTAMIENTO FOTOGRAFICO, QUE DE SE PRESENTA FIRMADO POR EL D.R.O. Y PROPIETARIO

2024 - 2027
DIRECCIÓN DE DESARROLLO URBANO SUSTENTABILIDAD, ORDENAMIENTO TERRITORIAL E IMAGEN

Arq. Rosa Ivette Portugal Cárdenas Directora de Desarrollo Urbano, Sustentabilidad, Ordenamiento Territorial e Imagen Urbana	C. Nora Aguilar P. Enlace Administrativo