Gobierno Municipal
CORONANGO
2024-2027
Tú confianza, nos lleva al progreso

FOLIO: 2832

DIRECCIÓN DE DESARROLLO URBANO, SUSTENTABILIDAD, ORDENAMIENTO TERRITORIAL E IMAGEN URBANA.

H. AYUNTAMIENTO DEL MUNICIPIO DE CORONANGO 2024-2027

CONSTANCIA DE ALINEAMIENTO Y NÚMERO OFICIAL

N° DE OFICIO: **ALI-929-2025.**

"COMERCIAL IAC" S.A. DE C.V., (ARRENDATARIO).

DATOS GENERALES							
CALLE:		**LATERAL AUTOPISTA MÉXICO PUEBLA KM 115**					
LOCAL:	**M-1**	MANZANA:	-	N° ACTUAL	**1001**	JUNTA AUXILIAR:	**SAN FRANCISCO OCOTLÁN**
MUNICIPIO:		**CORONANGO, PUEBLA.**					
SUPERFICIE:		**194.00 M2**				CUENTA PREDIAL	**U- 67568.**
MEDIDAS Y COLINDANCIAS:							
AL NORTE:		EN 15.07 M. COLINDA CON ACCESO Y PASILLO DE LA PLAZA.					
AL SUR:		EN 15.07 M. COLINDA CON LOCAL COMERCIAL.					
AL OESTE:		EN 12.75 M. COLINDA CON PASILLO DE LA PLAZA COMERCIAL.					
AL ESTE:		EN 12.75 M. COLINDA CON LOCAL COMERCIAL.					

ALINEAMIENTO Y NUMERO OFICIAL					
ESTA DIRECCIÓN POR MEDIO DEL AREA CORRESPONDIENTE SEÑALANDO					
CALLE:	**LATERAL AUTOPISTA MÉXICO PUEBLA KM 115**	N° OFICIAL:	**1001**	LOCAL:	**M-1**
FRACCIONAMIENTO O CONJUNTO HABITACIONAL		----			
MUNICIPIO:	**CORONANGO, PUEBLA.**	JUNTA AUXILIAR:	**SAN FRANCISCO OCOTLÁN**		
EL PREDIO SE UBICA EN: **ÁREA COMERCIAL**					

OBSERVACIONES PARTICULARES:

CONTRATO DE ARRENDAMIENTO SIMPLE FIRMADO POR ARRENDADOR: **PARQUES INDUSTRIALES DE PUEBLA S.A. DE C.V.**, ARRENDATARIO: **COMERCIAL IAC S.A. DE C.V.**, CON FECHA DE INICIO **01 DE SEPTIEMBRE DE 2021 AL 31 DE AGOSTO DE 2027.**

ACTA CONSTITUTIVA LIBRO NO. 661, INSTRUMENTO NO. 39,227, DE LA NOTARIA NO. 218, A CARGO DEL LIC. URIEL OLIVA SANCHEZ, DE FECHA 17 DE JULIO DE 2008, DEL DISTRITO JUDICIAL DE MÉXICO, D.F., INSCRITO EN EL REGISTRO PUBLICO DE LA PROPIEDAD Y DEL COMERCIO EL DÍA. 04 DE FEBRERO DE 2010.

PODER NOTARIAL, VOLUMEN NO. 699, ESCRITURA NO. 34659, DE LA NOTARIA NO. 65, A CARGO DEL LIC. JOSE LUIS MAZOY KURI, DE FECHA 01 DE JUNIO DE 2010, DEL DISTRITO JUDICIAL DEL ESTADO DE MÉXICO.

ESTE DOCUMENTO ES EXPEDIDO SOLO PARA TRAMITES DE USO DE SUELO ESPECIFICO Y/O LICENCIA DE FUNCIONAMIENTO.

EN CASO DE CONTROVERSIA JUDICIAL O ADMINISTRATIVA DERIVADO DE UN CONFLICTO ENTRE PARTICULARES, ESTE DOCUMENTO QUEDA SIN EFECTO Y SERÁ NULO DE PLENO DERECHO SIN NECESIDAD DE DECLARACIÓN ADMINISTRATIVA O JUDICIAL. AUNADO A LO ANTERIOR ESTA AUTORIDAD CARECE DE COMPETENCIA MATERIAL PARA INTERVENIR EN DISPUTAS DE INDOLE ESTRICTAMENTE CIVIL PRIVADA, POR LO QUE SE DESLINDA DE TODA RESPONSABILIDAD LEGAL Y MATERIAL, DEBIENDO RESOLVER EL CONFLICTO A TRAVÉS DE LAS INSTANCIAS LEGALES CORRESPONDIENTES.

VIGENCIA UN AÑO.
SEGÚN LO DISPUESTO EN LA LEY DE DESARROLLO URBANO SUSTENTABLE DEL ESTADO DE PUEBLA ART. 75 Y ART. 126 DE LA LEY DE ORDENAMIENTO TERRITORIAL Y DESARROLLO URBANO DEL ESTADO DE PUEBLA (LAS LICENCIAS, PERMISOS Y AUTORIZACIONES TENDRÁN LA VIGENCIA QUE DETERMINE LA AUTORIDAD QUE LAS EXPIDE Y PODRÁN SER PRORROGADAS POR DETERMINACIÓN DE ESTE).

Con fundamento en lo dispuesto en los artículos 27 párrafo tercero y 115 fracción V, inciso f); CONSTITUCIÓN POLITICA DE LOS ESTADOS UNIDOS MEXICANOS; 11, fracciones I, II, III, XI y XV, 43, 47, 48 y 59 LEY GENERAL DE ASENTAMIENTOS HUMANOS, ORDENAMIENTO TERRITORIAL Y DESARROLLO URBANO; 105, fracción IV, incisos a), d), e) y f) CONSTITUCIÓN POLÍTICA DEL ESTADO LIBRE Y SOBERANO DE PUEBLA: 12 fracción IV, 16 fracciones XVIII y XXIV, 86, 87, 90, 102, 119, 120, 122, 123 fracción IV, 124, 126 y 133 fracciones IV y VI LEY DE ORDENAMIENTO TERRITORIAL Y DESARROLLO URBANO DEL ESTADO DE PUEBLA; 13 fracciones IV, VI y VII, 67, 68, 70, 71, 72, 73, 74 y 75 LEY DE DESARROLLO URBANO SUSTENTABLE DEL ESTADO DE PUEBLA; 8 fracción III, 9 y 12 fracciones I, II y III LEY DE FRACCIONAMIENTOS Y ACCIONES URBANISTICAS DEL ESTADO LIBRE Y SOBERANO DE PUEBLA; 254, 255 REGLAMENTO DE CONSTRUCCIONES PARA EL ESTADO DE PUEBLA; 78, fracciones XLI, XLII y XLIII LEY ORGÁNICA MUNICIPAL; 14 fracciones I incisos a), b), c), d), e), f), g) numeral 1, II incisos a), b), c) y d) LEY DE INGRESOS DEL MUNICIPIO DE CORONANGO PARA EL EJERCICIO FISCAL 2026; 1277 fracción I inciso a), 1278, 1279 fracciones V y LXXVII, 1280 fracción II, 1283 fracción XXII, 1327, 1595 fracción XVIII, 1665 y 1666 REGLAMENTO DE ORDEN Y JUSTICIA CÍVICA MUNICIPAL DE CORONANGO, PUEBLA; PROGRAMA MUNICIPAL DE DESARROLLO URBANO SUSTENTABLE DE CORONANGO Publicado con fecha 08 de junio de 2018. PROGRAMA MUNICIPAL DE DESARROLLO URBANO SUSTENTABLE DE CORONANGO, ARTÍCULO 14 FRACCIÓN I y II DE LA LEY DE INGRESOS DEL MUNICIPIO DE CORONANGO PARA EL EJERCICIO FISCAL VIGENTE 2026; LAS LICENCIAS, PERMISOS Y AUTORIZACIONES QUE EXPIDA LA AUTORIDAD MUNICIPAL, LOS DATOS PERSONALES RECABADOS SERÁN PROTEGIDOS, INCORPORADOS Y TRATADOS DE ACUERDO CON LO ESTABLECIDO EN LOS ARTÍCULOS 1, 26, 30 Y 31 DE LA LEY GENERAL DE PROTECCIÓN DE DATOS PERSONALES EN POSESIÓN DE SUJETOS OBLIGADOS; Y 7 DE LOS LINEAMIENTOS GENERALES DE PROTECCIÓN DE DATOS PERSONALES PARA EL SECTOR PÚBLICO. ASÍ MISMOS SE LE INFORMA QUE SUS DATOS NO PODRÁN SER DIFUNDIDOS SIN SU CONSENTIMIENTO EXPRESO, SALVO LAS EXCEPCIONES PREVISTAS EN LA LEY.

Gobierno Municipal
CORONANGO
2024 - 2027
Tu confianza, nos lleva al progreso

11 DE FEBRERO DE 2026
ALINEAMIENTO N° DE OFICIO: ALI-929-2025

CROQUIS ESQUEMATICO

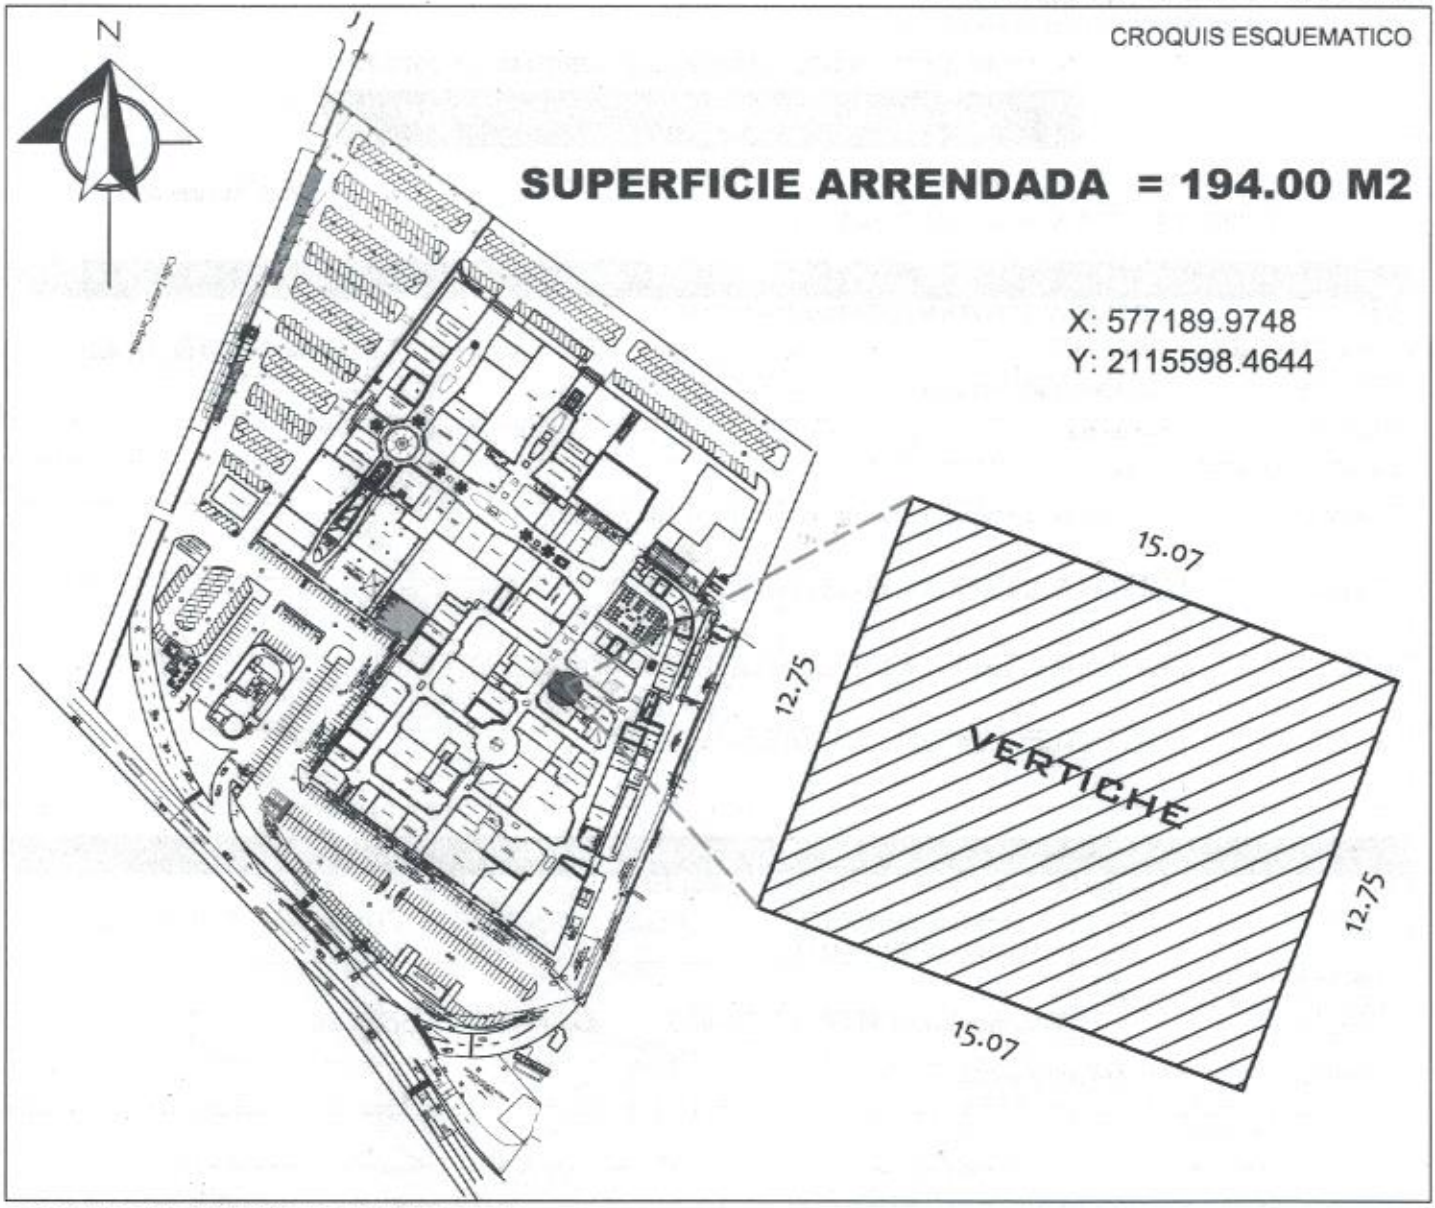

OBSERVACIONES ALINEAMIENTO Y NUMERO OFICIAL

-TÉCNICO URBANÍSTICO - NO CONSTITUYE NI CERTIFICA PROPIEDAD O POSESION CONSTANCIA DE APEO Y DESLINDE.
-SE EXPIDE SIN PERJUICIO A TERCEROS.
-SUPERFICIE, MEDIDAS Y COLINDANCIAS SON RESPONSABILIDAD DEL INTERESADO.
-SE EXPIDE PARA CONOCIMIENTO DE NOMENCLATURA.
-DOCUMENTO DE CARÁCTER TÉCNICO.
-INFORMACIÓN PROPORCIONADA BAJO PROTESTA DE DECIR VERDAD POR EL INTERESADO.
-SUJETO A LAS DISPOSICIONES TÉCNICO NORMATIVAS REGLAMENTARIAS APLICABLES EN MATERIA DE PLANEACIÓN DE DESARROLLO URBANO.
-ESTE ALINEAMIENTO ES EXPEDIDO EN BASE A UN CROQUIS PRESENTADO Y FIRMADO POR EL INTERESADO Y D.R.O.
-EN CASO DE EXISTIR ALGUNA RECLAMACIÓN, INCONSISTENCIA O ILEGALIDAD QUE DETECTE CATASTRO, R.P.P, EL NOTARIO PUBLICO, EL ADQUIRIENTE O CUALQUIER DEPENDENCIA ADMINISTRATIVA SERÁN EXCLUSIVA RESPONSABILIDAD DEL SOLICITANTE O EN SU CASO EL PROPIETARIO.
-EL PRESENTE ALINEAMIENTO SE REALIZA CONFORME A LA INFORMACIÓN PROPORCIONADA POR EL INTERESADO, POR LO QUE CUALQUIEER ACLARACION O CAMBIO SERA UNICAMENTE RESPONSABNILIDAD DEL MISMO
-ESTE CROQUIS Y No. OFICIAL SE REALIZA Y SE EXPIDE SOLAMENTE PARA TRAMITES DE USO DE SUELO ESPECIFICO Y LICENCIA DE FUNCIONAMIENTO.

Lic. Jesús Morales Garduño. Encargado de Despacho de la Dirección de Desarrollo Urbano, Sustentabilidad, Ordenamiento Territorial e Imagen Urbana	C. Nora Aguilar P. Enlace Administrativo